



514 Hillcrest Industrial Blvd
Macon, GA 31204
P (478) 757-1606
F (478) 757-1608
Terracon.com

February 10, 2023

River Valley Regional Commission
710 Front Avenue
Columbus, Georgia 31901-2995

Attn: Ms. Laura Schneider
P: (706) 256-2910
E: lschneider@rivervalleyrc.org

RE: Wetlands and Waters of the United States Field Determination
RVRC Brownfield Assessment Grant Services
Swett Avenue Tract
Swett Avenue
Americus, Sumter County, Georgia
Terracon Job No. HP217183, Task 3C.14B

Dear Ms. Schneider:

Terracon Consultants, Inc (Terracon) is pleased to present this evaluation of our wetland delineation services for the Swett Avenue site located off Swett Avenue Americus, Sumter County, Georgia. The subject property consists of approximately 104.0 acres and is an undeveloped tract of land. The site vicinity consists predominately of commercial properties and wooded land. The subject scope of work was to delineate all wetlands and waters of the United States that may be located within the project area boundaries.

The field survey for the wetland delineation and assessment, on the above referenced project area in Unadilla, Georgia, was conducted on February 7 and 8, 2023. Prior to visiting the site, background research was conducted and consisted of locating and reviewing aerial photographs, topographic maps, U.S. Fish and Wildlife Service (USFWS) National Wetlands Inventory (NWI) maps, U.S. Geological Survey (USGS) Topographic Maps, soil data from the Natural Resources Conservation Service (NRCS), and/or other related available databases. The data analysis assisted Terracon in identifying potential aquatic resources and jurisdictional features on the site.

In accordance with the Corps of Engineers Wetland Delineation Manual (1987) and Regional Supplement, the standard delineation protocol was used in conjunction with a modified protocol. The modified protocol implements the following parameters to determine boundary lines between upland and wetland areas: These parameters include but are not limited to, plant community transitions, significant topographic changes, hydrology, and test holes for indication of wetland soils. During the assessment, if a change in one of the parameters was observed, then all parameters were tested, per the standard delineation protocol, to classify the area as either upland or a wetland. The interaction of hydrology, vegetation, and soil results in the development of characteristics unique to wetlands. All three parameters must be present for wetlands to occur.

Terracon delineated approximately 61.47 acres of wetland, 1,862 linear feet (0.42 acres) of perennial stream, and 69 linear feet (0.01 acres) of ephemeral stream on the subject property. In Terracon's

opinion, there are jurisdictional wetlands on the subject property and any impact to these areas would need a permit from the U.S. Army Corps of Engineers as well as possible compensatory mitigation.

Terracon appreciates the opportunity to be of service to you. If you have any questions, or need further assistance, please do not hesitate to call.


Sincerely,
TERRACON CONSULTANTS, INC.

A handwritten signature in blue ink that reads 'Melissa LeCroy'.

Melissa LeCroy
Field Scientist

A handwritten signature in blue ink that reads 'Mary Brooks'.

Mary A. Brooks, PWS #2075
Environmental Planning Manager

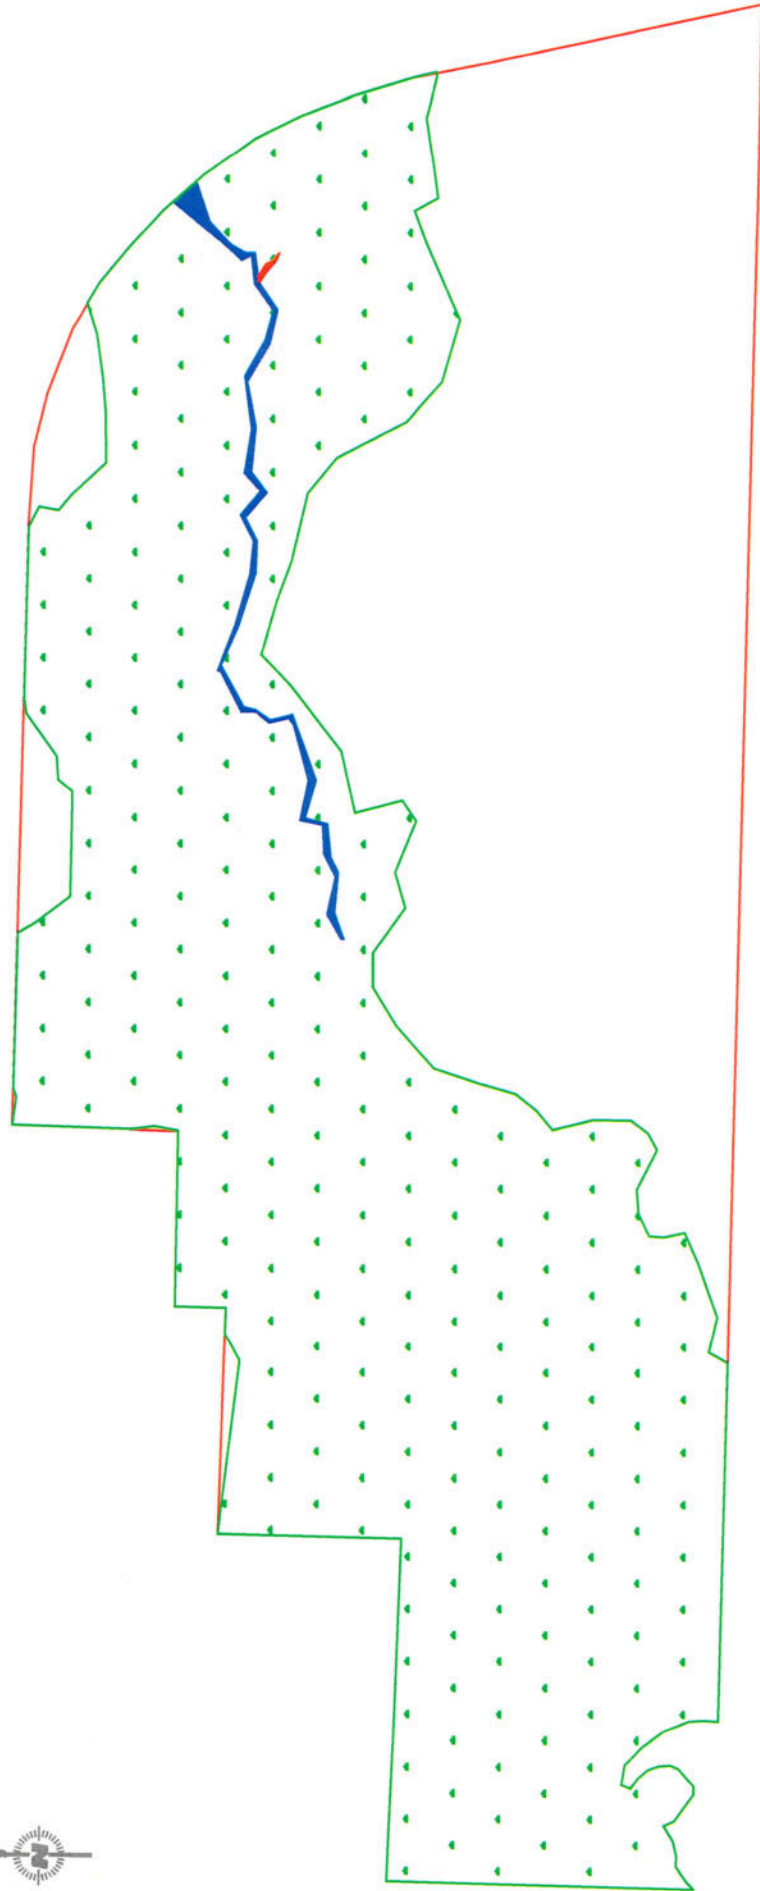

Legend

- = Approximate Project Boundary (~103.91 acres)
- = Wetland Area (~61.47 acres; 59.16%)
- = Perennial Stream (~1,862 LF; 0.42 acres; 0.40%)
- = Ephemeral Stream (~69 LF; 0.01 acres; 0.009%)

Project Manager:	KS
Drawn By:	ML
Checked By:	MB
Approved By:	JC

Project No.:	HP217183
Scale:	A1; 1:400
File Name:	3C_14B
Date:	FEB 2023

**Terracon**
Explore with us


514 Hillcrest Industrial Boulevard
Macon, Georgia 31204

Wetland Delineation Map

RVRC Brownfield Assessment Grant Services
Sweett Avenue Site
Delineated 2/7-2/8/2023
Sweett Avenue
Americus, Georgia

Exhibit

1

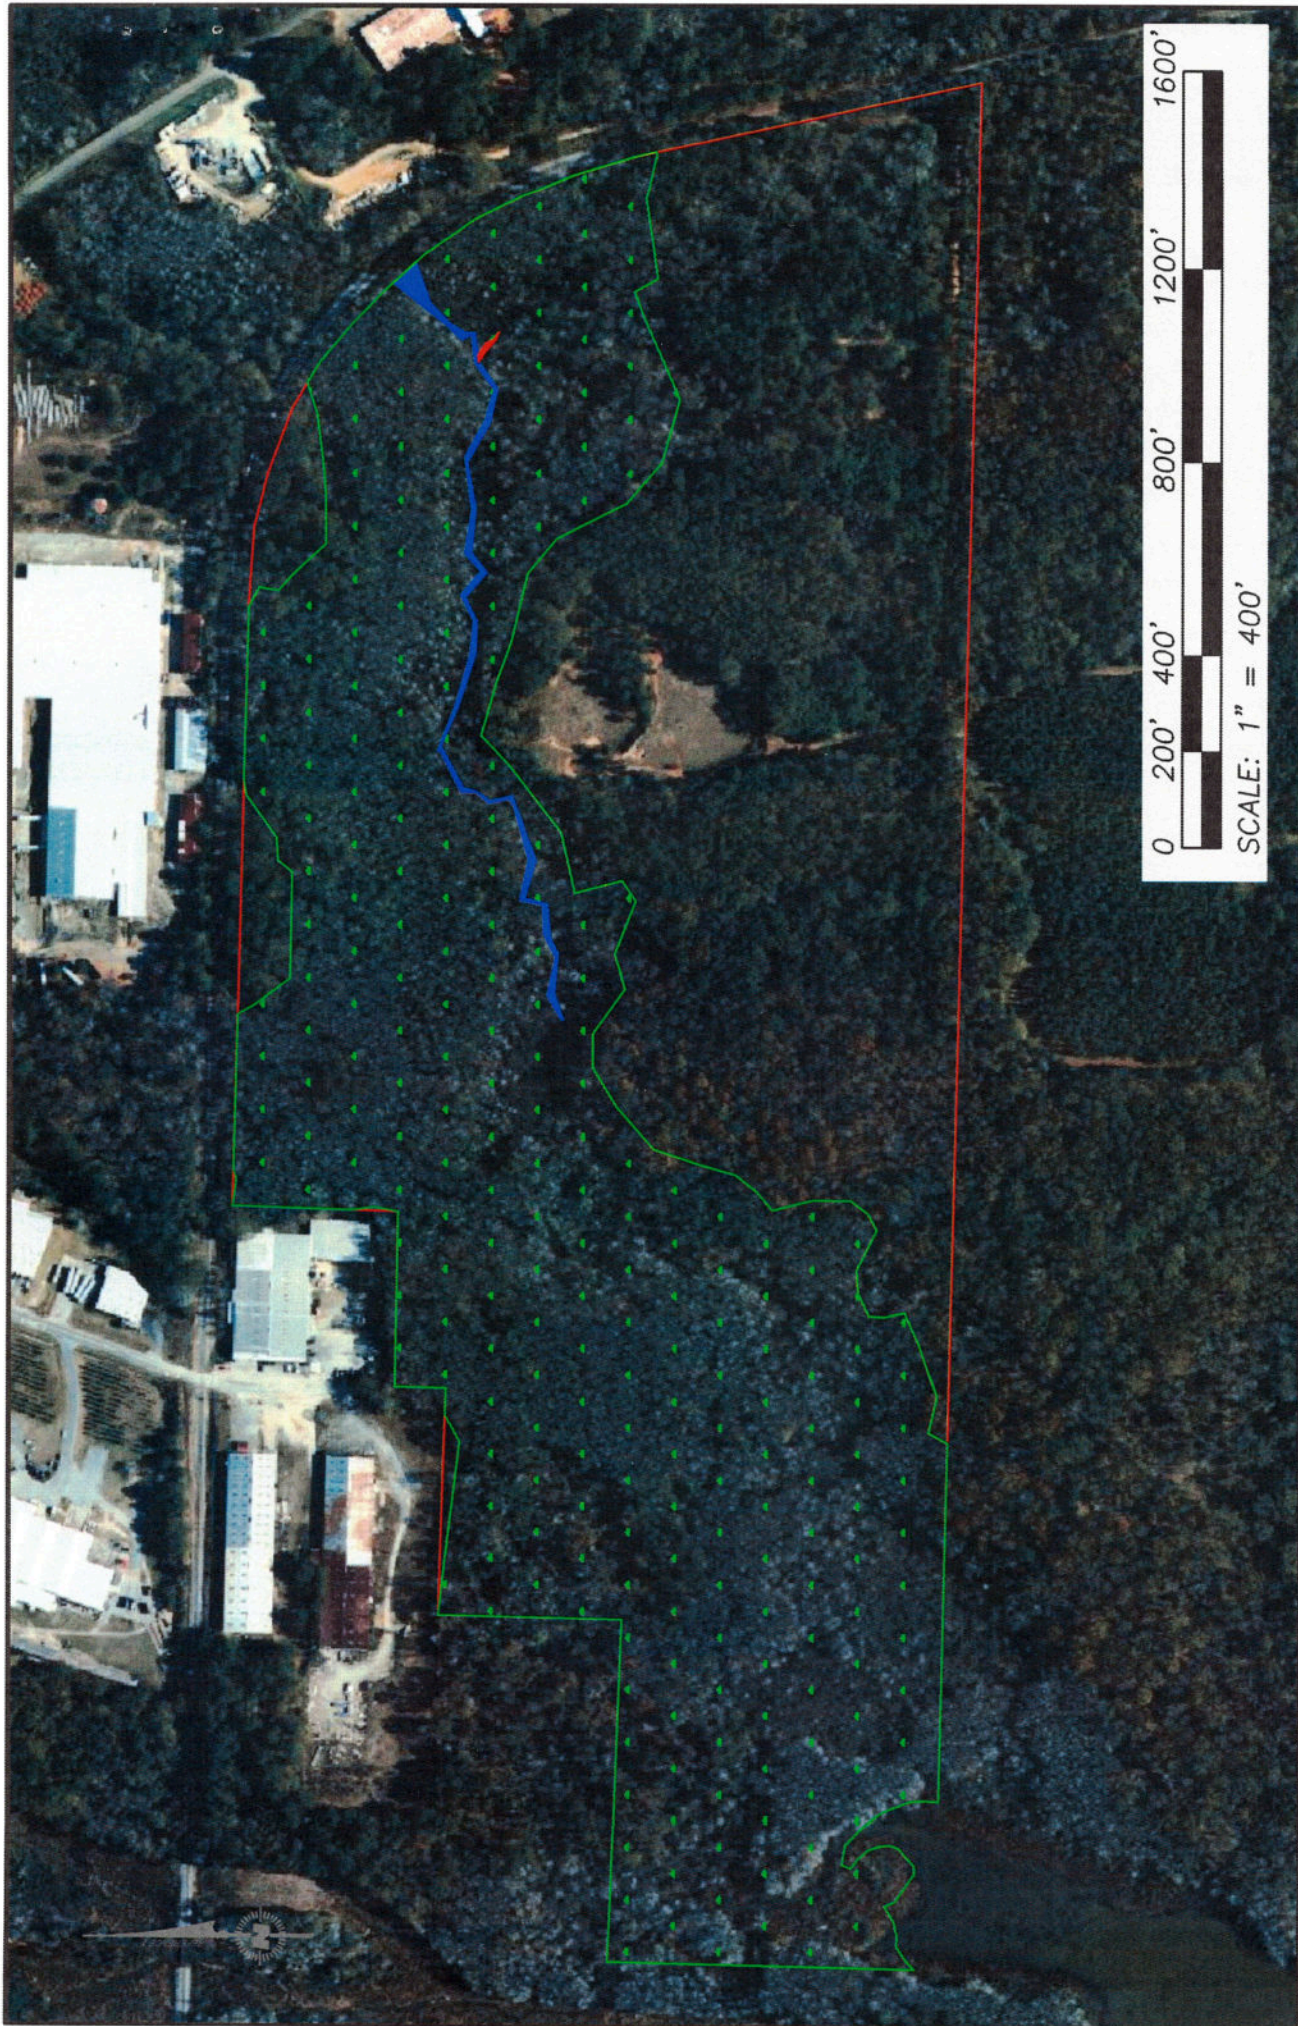

Legend

- = Approximate Project Boundary (~103.91 acres)
- = Wetland Area (~61.47 acres; 59.16%)
- = Perennial Stream (~1,862 LF; 0.42 acres; 0.40%)
- = Ephemeral Stream (~69 LF; 0.01 acres; 0.009%)

Project Manager:	KS
Drawn By:	ML
Checked By:	MB
Approved By:	JC

Project No.:	HP217183
Scale:	A1; 1:400
File Name:	3C_14B
Date:	FEB 2023



514 Hillcrest Industrial Boulevard
Macon, Georgia 31204

Wetland Delineation Map

RVRC Brownfield Assessment Grant Services
Sweett Avenue Site
Delineated 2/7-2/8/2023
Sweett Avenue
Americus, Georgia

Exhibit

1